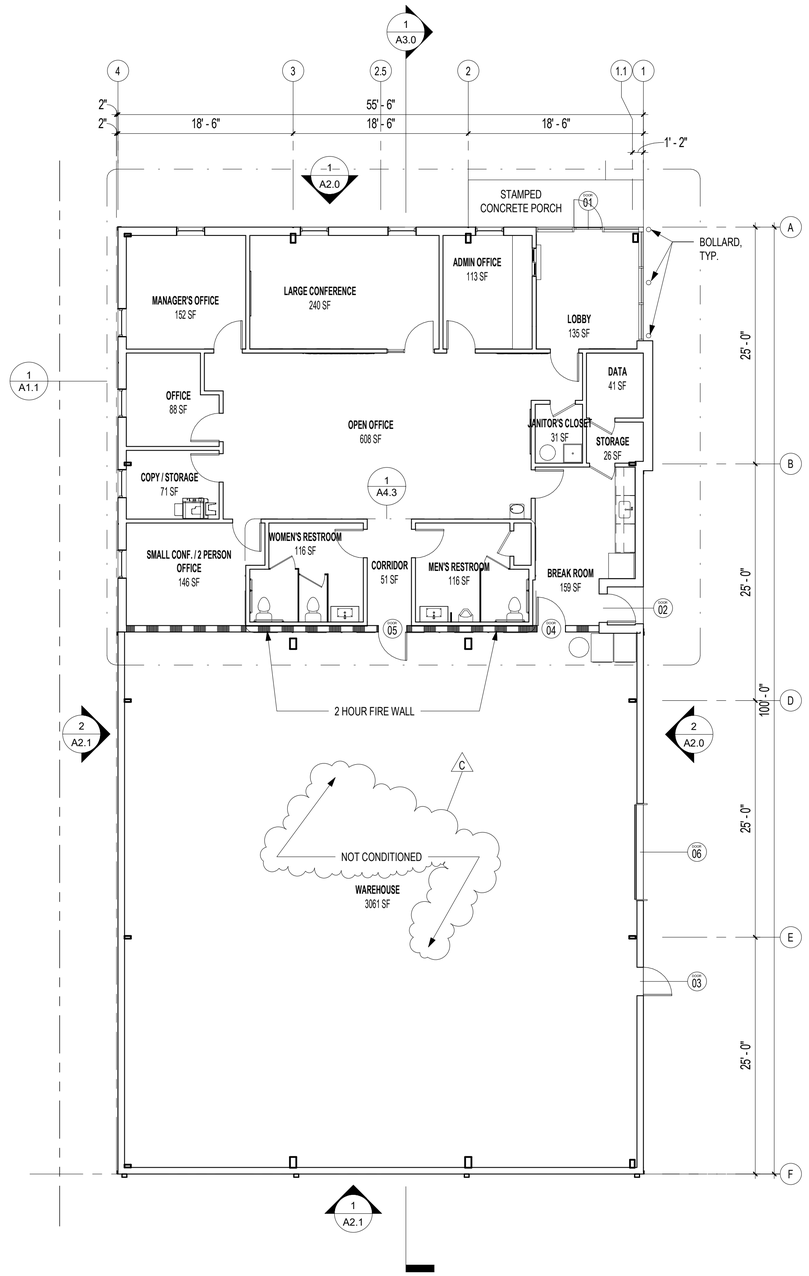

OVERALL FLOOR PLAN 1

1/8" = 1'-0"

DUNCAN ARCHITECTS

TRDI OFFICE AND WAREHOUSE

941 W. SHARM DR.
PHARR, TX 78577

OWNER
TRDI
425 SOLEDAD, SUITE 800
SAN ANTONIO, TX 78205
210-572-0402

ARCHITECT
DUNCAN ARCHITECTS LLC
804 PECAN BLVD, SUITE 113
McALLEN, TX 78501
956-443-3755

CIVIL ENGINEER
RGV STRATA
4900 TEXAN ROAD
MISSION, TX 78574
956-802-7328

MEP ENGINEER
RO ENGINEERING, PLLC
2705 E. DAVIS RD.
EDINBURG, TX 78540
(956) 292-3336

LANDSCAPE ARCHITECT
HEFFNER DESIGN TEAM
4100 N. 22ND STREET
McALLEN, TX 78504
956-540-7850

STRUCTURAL ENGINEER
ATLAS ENGINEERING
CONSULTANTS, LLC
500 SOUTH 11TH STREET
McALLEN, TX 78501
956-379-3857

P.E.M.B. SUPPLIER & E.O.R.

REV.	DESCRIPTION	DATE
A	90% CONSTRUCTION DOCUMENTS	02/02/2024
B	CONSTRUCTION DOCUMENTS FOR BIDDING	02/16/2022
C	BIDDING REVISION 1	02/28/2024

FEBRUARY 16TH, 2024
CONSTRUCTION DOCUMENTS FOR BIDDING

NOT FOR REGULATORY APPROVAL, PERMITTING, OR CONSTRUCTION

SCALE 1/8" = 1'-0"
DRAWN BY: DUNCAN ARCHITECTS
DATE: 16 FEBRUARY 2024

OVERALL FLOOR PLAN

A1.0