© 2017 FKP Architects, Inc. All rights reserved. No part of this document may be reproduced or utilized in any form without prior written authorization of FKP Architects, Inc.

GENERAL NOTES TO PLANS

EXISTING
NEW
AREA NOT IN SCOPE

LEGEND
N.T.S.

A. INFORMATION SHOWN OR REFERENCED ON ENLARGED AND/OR 1/4" SCALE DRAWINGS WILL GENERALLY NOT BE SHOWN ON THE SMALLER SCALE DRAWINGS.
B. PARTITION TYPES ARE SCHEDULED ON PLANS BY NUMBER. SEE THE "GENERAL NOTES TO PARTITION TYPES" ON A11.1 AND PARTITION TYPES ON SHEET A11.1 FOR THE DEFINITION OF PARTITION TYPE REFERENCES KEYED ON PLANS.
C. FIELD COORDINATE ALL FIELD ROUTED PIPE, CONDUIT RUNS, ETC., WITH LOCATIONS OF RECESSED ACCESSORIES AND EQUIPMENT. IN THE EVENT OF A CONFLICT, ACCESSORY LOCATIONS TAKE PRECEDENCE.
D. CLOSE ALL JOINTS BETWEEN PLUMBING FIXTURES/ACCESSORIES AND DISSIMILAR MATERIALS W/SEALANT (I.E. BETWEEN SINKS AND COUNTERTOPS, TOILET FIXTURES AND ACCESSORIES TO WALL, ETC.)
E. CABINET NUMBERS NOTED ON ENLARGED PLANS REFER TO CABINET COMPONENT NUMBERS, FIXTURES, ACCESSORIES, ETC. THAT ARE DEFINED OR ELEVATED ON SHEET A9.0A UNLESS SPECIFIC DETAIL REFERENCES ARE KEYED.
F. PLAN DIMENSIONS ARE TO FINISHED FACE OF PARTITIONS AND GENERALLY ARE TIED TO A COLUMN CENTERLINE UNLESS SPECIFICALLY SHOWN CENTERED ON A PARTICULAR BUILDING ELEMENT I.E. A CHASE WALL, WINDOW MULLION, ETC.
O. STANDARD EQUIPMENT WALL MOUNTING HEIGHTS, SEE DETAIL A2/A6.1.
P. MEDICAL EQUIPMENT WALL MOUNTING HEIGHTS, SEE DETAIL D3/A6.2.
Q. FIRE PROTECTION EQUIPMENT WALL MOUNTING HEIGHTS, SEE DETAIL A6/A6.1.
R. COMMUNICATION EQUIPMENT WALL MOUNTING HEIGHTS, SEE DETAIL D6/A6.2.
S. EQUIPMENT MOUNTING HEIGHTS AT COUNTERTOPS, SEE DETAIL B3/A6.2.
T. EQUIPMENT MOUNTING HEIGHTS AT DESKTOPS, SEE DETAIL B4/A6.2.

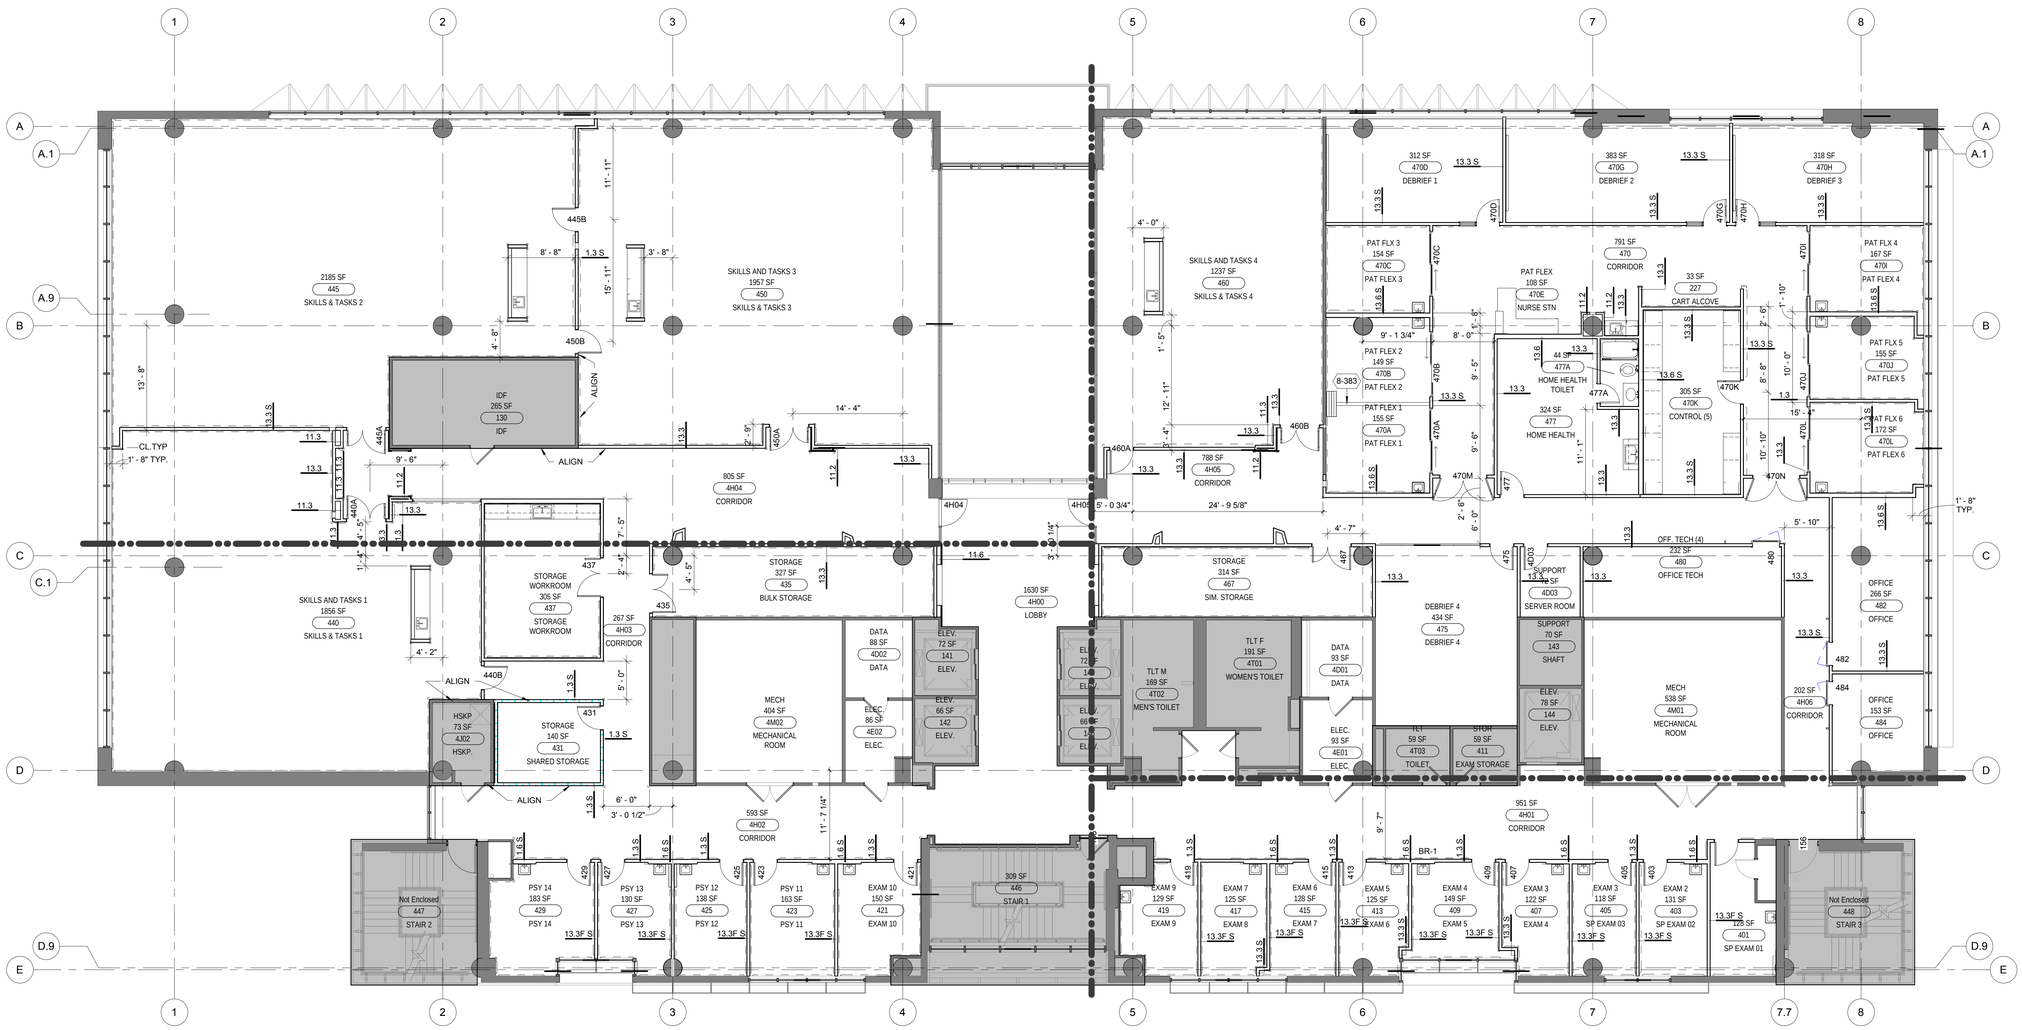

A6 Level 4 - FLOOR PLAN
1/8" = 1'-0"

FKP
Houston | Dallas | Columbus

ARCHITECT OF RECORD

CYNTHIA D. WALSTON

DATE: 07/02/2018

REVISIONS

PROJECT NAME

UTHealth
Jane and Robert Cizik School of Nursing
The University of Texas Health Science Center at Houston

SIMULATION LAB

PROJECT NUMBER

045017.0000
CIP 1601

ISSUE

ISSUE FOR CONSTRUCTION

DATE

07/02/2018

DRAWING TITLE

LEVEL 4 OVERALL FLOOR PLAN

DRAWING NUMBER

A2.1