© 2017 FKP Architects, Inc. All rights reserved. No part of this document may be reproduced or utilized in any form without prior written authorization of FKP Architects, Inc.

EXISTING
NEW
AREA NOT IN SCOPE

LEGEND
N.T.S.

NOTES TO SHEET

1-101 SEE EXAMROOM 403 FOR TYPICAL ELEVATIONS
9-802 ACOUSTICAL BLANKET.

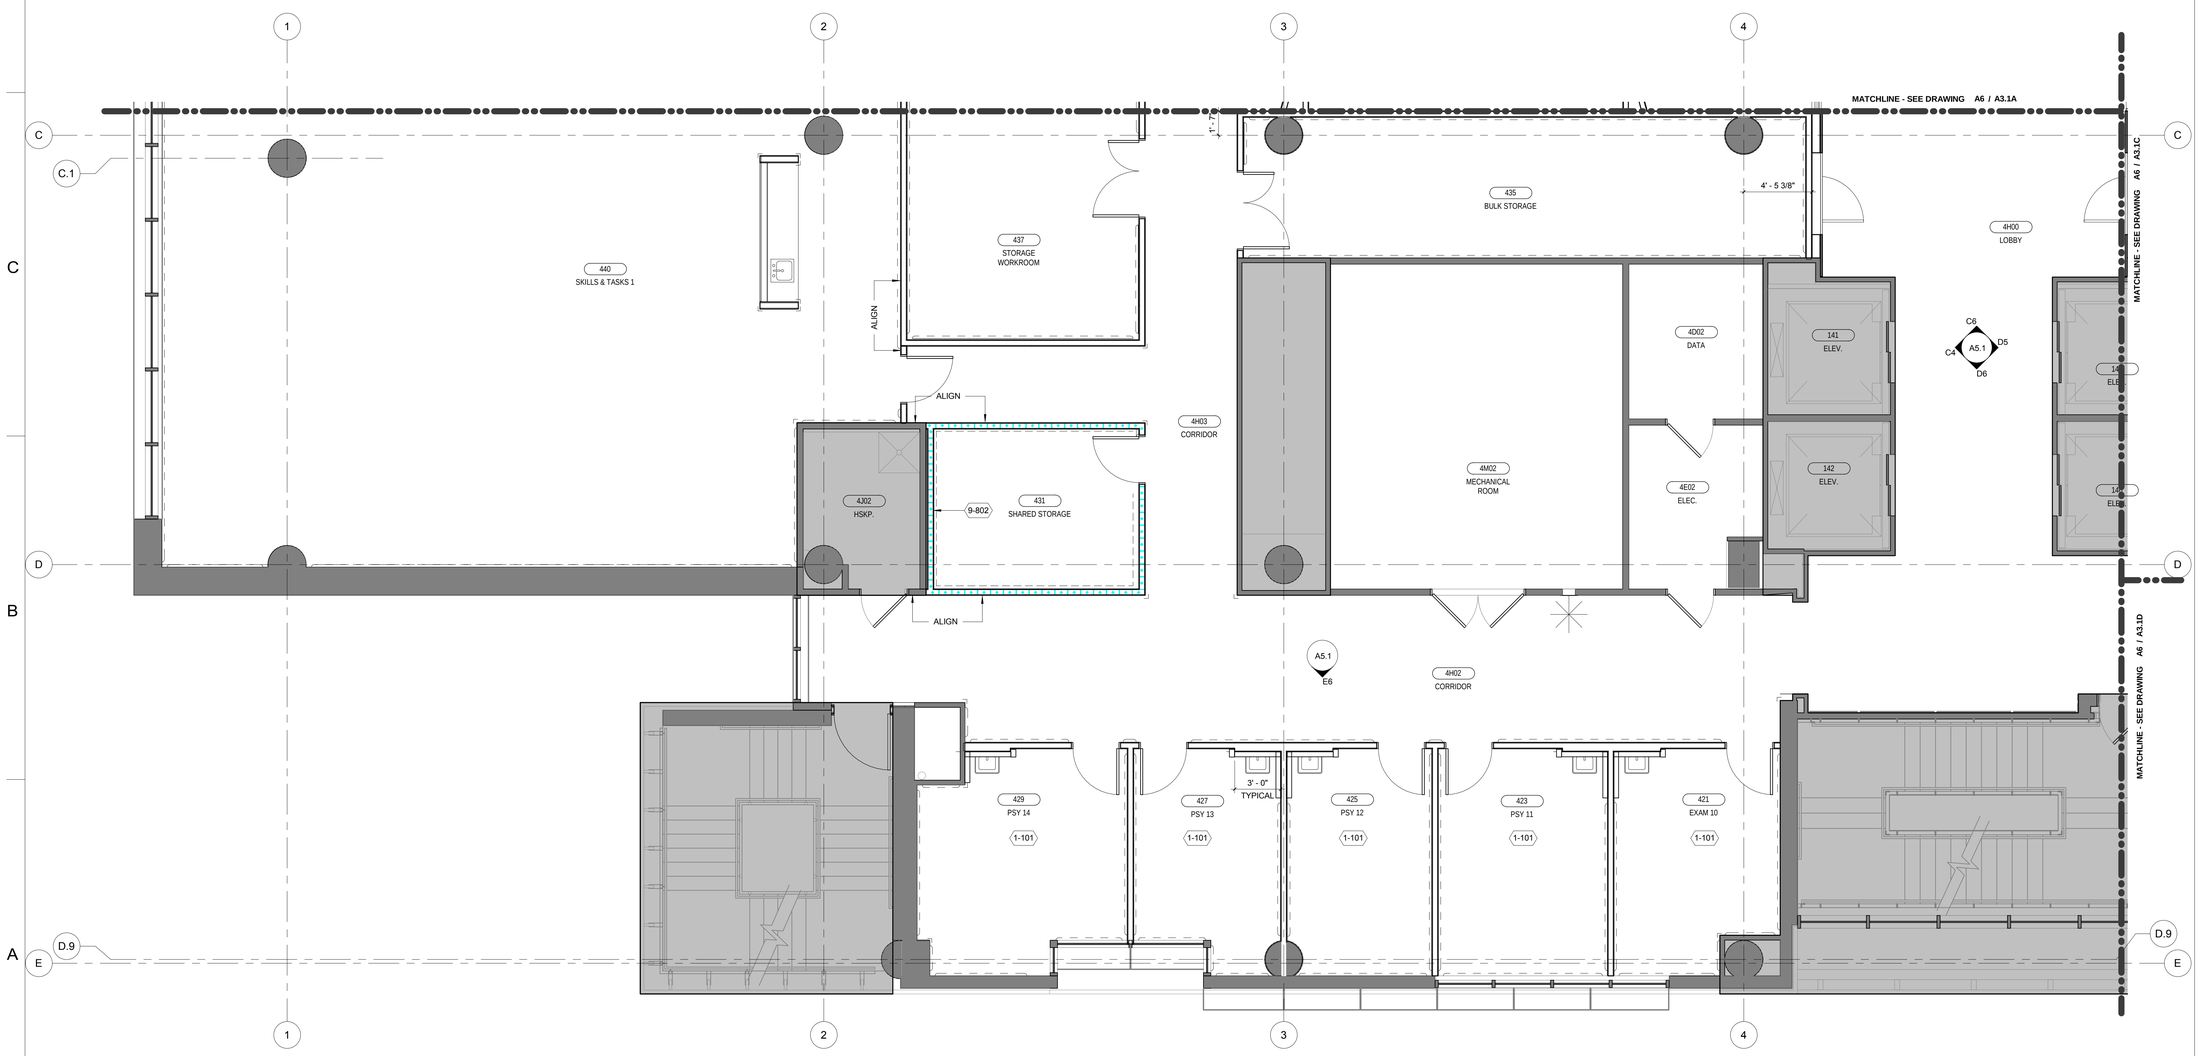

A6 Level 4 - FLOOR PLAN NW
1/4" = 1'-0"

FKP
Houston | Dallas | Columbus

ARCHITECT OF RECORD

CYNTHIA D. WALSTON

DATE: 07/02/2018

REVISIONS

PROJECT NAME

UTHealth
Jane and Robert Cizik School of Nursing
The University of Texas Health Science Center at Houston

SIMULATION LAB

PROJECT NUMBER
045017.0000
CIP 1601

ISSUE
ISSUE FOR CONSTRUCTION

DATE
07/02/2018

DRAWING TITLE
LEVEL 4 ENLARGED PLANS

DRAWING NUMBER
A3.1B