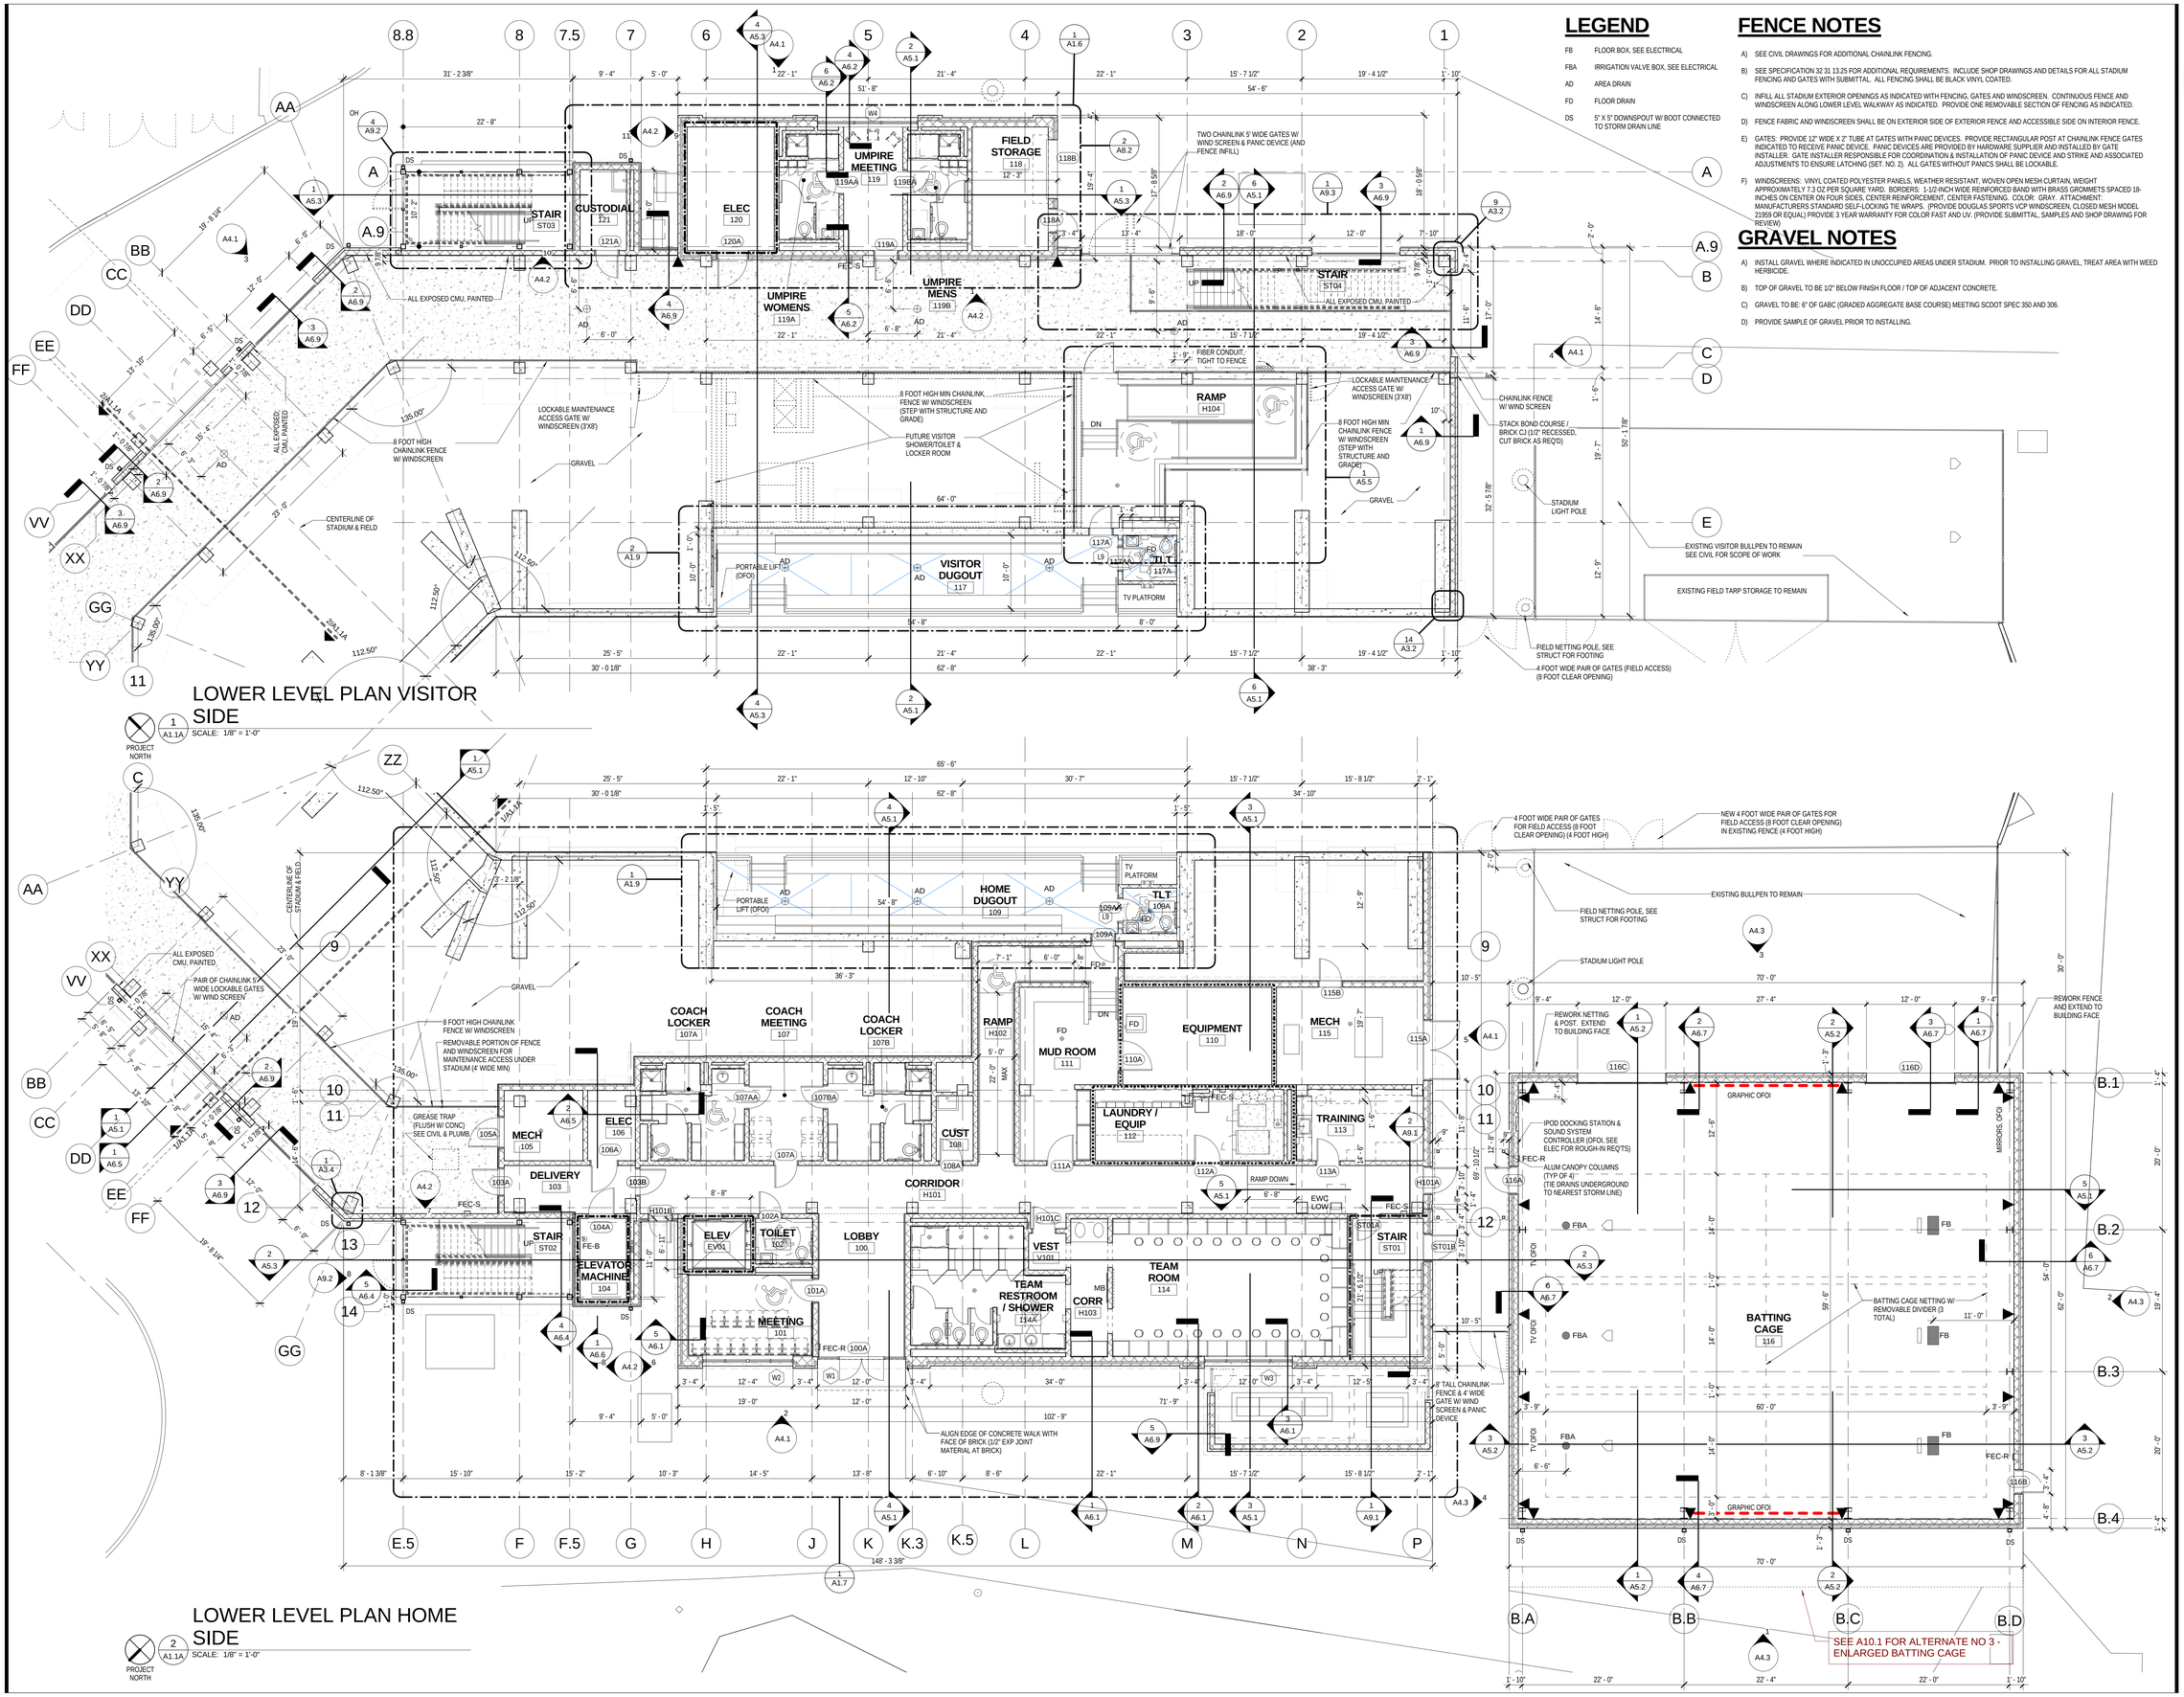

LEGEND

FB	FLOOR BOX, SEE ELECTRICAL
FBA	IRRIGATION VALVE BOX, SEE ELECTRICAL
AD	AREA DRAIN
FD	FLOOR DRAIN
DS	5" X 5" DOWNSPOUT W/ BOOT CONNECTED TO STORM DRAIN LINE

FENCE NOTES

A) SEE CIVIL DRAWINGS FOR ADDITIONAL CHAINLINK FENCING.

B) SEE SPECIFICATION 32 31 13.25 FOR ADDITIONAL REQUIREMENTS. INCLUDE SHOP DRAWINGS AND DETAILS FOR ALL STADIUM FENCING AND GATES WITH SUBMITTAL. ALL FENCING SHALL BE BLACK VINYL COATED.

C) INFILL ALL STADIUM EXTERIOR OPENINGS AS INDICATED WITH FENCING, GATES AND WINDSCREEN. CONTINUOUS FENCE AND WINDSCREEN ALONG LOWER LEVEL WALKWAY AS INDICATED. PROVIDE ONE REMOVABLE SECTION OF FENCING AS INDICATED.

D) FENCE FABRIC AND WINDSCREEN SHALL BE ON EXTERIOR SIDE OF EXTERIOR FENCE AND ACCESSIBLE SIDE ON INTERIOR FENCE.

E) GATES: PROVIDE 12" WIDE X 2" TUBE AT GATES WITH PANIC DEVICES. PROVIDE RECTANGULAR POST AT CHAINLINK FENCE GATES INDICATED TO RECEIVE PANIC DEVICE. PANIC DEVICES ARE PROVIDED BY HARDWARE SUPPLIER AND INSTALLED BY GATE INSTALLER. GATE INSTALLER RESPONSIBLE FOR COORDINATION & INSTALLATION OF PANIC DEVICE AND STRIKE AND ASSOCIATED ADJUSTMENTS TO ENSURE LATCHING (SET. NO. 2). ALL GATES WITHOUT PANICS SHALL BE LOCKABLE.

F) WINDSCREENS: VINYL COATED POLYESTER PANELS, WEATHER RESISTANT, WOVEN OPEN MESH CURTAIN, WEIGHT APPROXIMATELY 7.3 OZ PER SQUARE YARD. BORDERS: 1-1/2-INCH WIDE REINFORCED BAND WITH BRASS GROMMETS SPACED 18-INCHES ON CENTER ON FOUR SIDES. CENTER REINFORCEMENT, CENTER FASTENING. COLOR: GRAY. ATTACHMENT: MANUFACTURERS STANDARD SELF-LOCKING TIE WRAPS. (PROVIDE DOUGLAS SPORTS VCP WINDSCREEN, CLOSED MESH MODEL 21959 OR EQUAL) PROVIDE 3 YEAR WARRANTY FOR COLOR FAST AND UV. (PROVIDE SUBMITTAL, SAMPLES AND SHOP DRAWING FOR REVIEW)

GRAVEL NOTES

A) INSTALL GRAVEL WHERE INDICATED IN UNOCCUPIED AREAS UNDER STADIUM. PRIOR TO INSTALLING GRAVEL, TREAT AREA WITH WEED HERBICIDE.

B) TOP OF GRAVEL TO BE 1/2" BELOW FINISH FLOOR / TOP OF ADJACENT CONCRETE.

C) GRAVEL TO BE: 6" OF GABC (GRADED AGGREGATE BASE COURSE) MEETING SCDOT SPEC 350 AND 306.

D) PROVIDE SAMPLE OF GRAVEL PRIOR TO INSTALLING.

QUACKENBUSH
ARCHITECTS + PLANNERS

1217 Hampton Street T: 803.771.2999
Columbia, SC 29201 F: 803.771.2858

CHA

III Winners Circle T: 518.453.4500
Albany, NY 12205 F: 518.458.1735

CORPORATE SEAL

STATE OF SOUTH CAROLINA
QUACKENBUSH ARCHITECTS + PLANNERS LLC
Columbia, SC
No. 100028
REGISTERED ARCHITECTS

A/E SEAL

STATE OF SOUTH CAROLINA
BRENDA HALLER
Columbia, SC
6198
REGISTERED ARCHITECT

PROJECT TITLE

UNIVERSITY OF SOUTH CAROLINA

SOFTBALL STADIUM CONSTRUCTION

BID SET

Conditions of Use: This drawing and the design thereon are the property of Quackenbush Architects + Planners. The reproduction, copying, or use of this drawing without the written consent of Quackenbush Architects + Planners is prohibited and any infringement will be subject to legal action.

REVISIONS

NO	REVISION	DATE

SHEET INFORMATION	
Date	03.16.12
Project No.	11.122.00
Scale	1/8" = 1'-0"
Drawn By	BLH
Checked By	BLH
State Project No.	H27-6088-MJ

TITLE

LOWER LEVEL ENLARGED PLANS

SHEET NO.

A1.1A

4/5/2012 11:13:54 AM